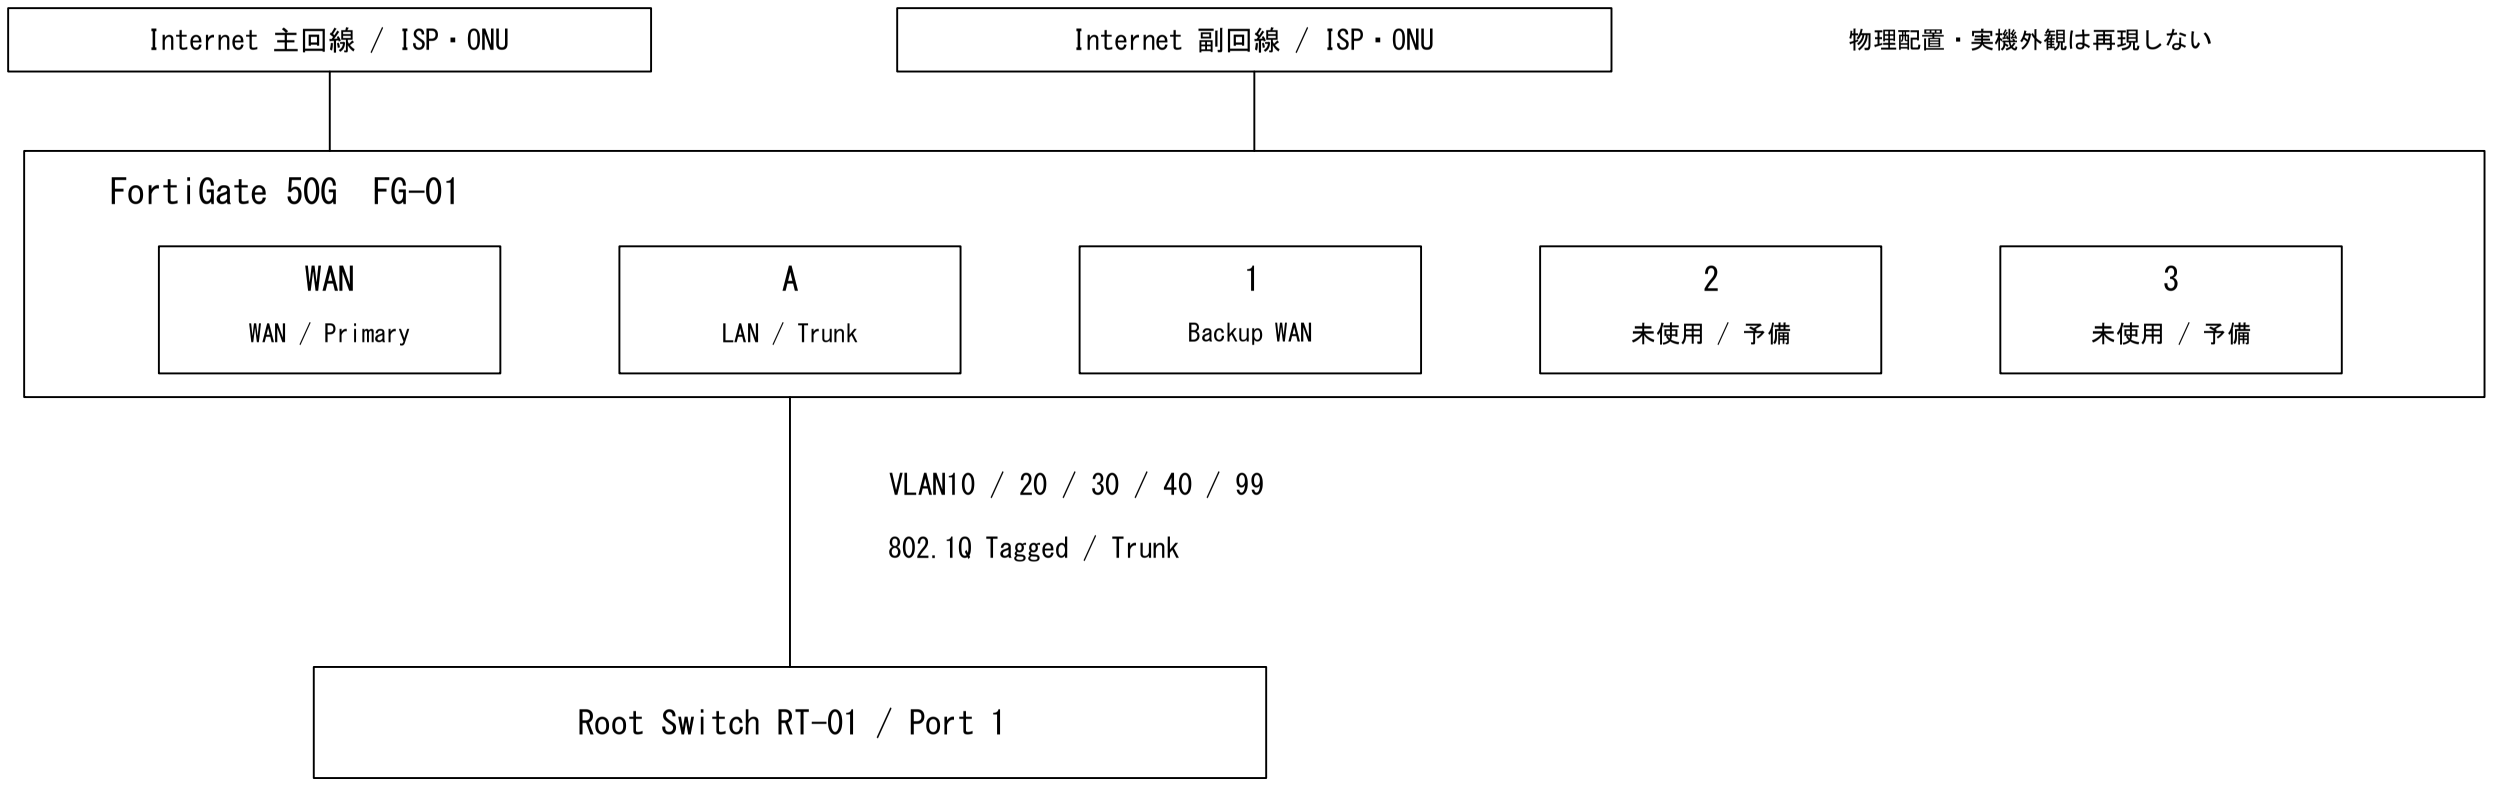


管理はVLAN99 MGMT経由。専用管理ポートは追加しない。副回線方式・SD-WAN設定は未確定。

Port No.	接続先	用途	VLAN	種別	備考
WAN	ISP / ONU 主回線	Internet主回線	WAN（非VLAN）	WAN	Primary
A	Root Switch RT-01 / P1	社内LAN接続	10 / 20 / 30 / 40 / 99	Trunk	802.1Q Tagged
1	ISP / ONU 副回線	Internet副回線	WAN（非VLAN）	WAN	Backup / 将来SD-WAN利用可能
2	未接続	将来拡張	-	未使用	予備
3	未接続	将来拡張	-	未使用	予備

FortiGate：Default Gateway / VLAN Routing / Firewall / NAT / VPN。VLAN間通信はFortiGate経由。

WAN側IP・Gateway・方式は回線契約仕様により決定。副回線は今回のPort設計上の想定で、回線契約は未定。

VPNは指定NAS（NAS-01 / 192.168.20.20）の必要通信のみ許可。ACL一覧のNAS NS-01と同一機器。

未使用Port 2・3：未接続 / 将来拡張用。ルーティング機能はRoot・Branchへ分散しない。

TITLE			PAGE
IT/OTネットワーク サンプル　Port図（FG-01 / 模式図）			01 / 03
SCALE	DATE	DRW No.	REV.
NTS	2026-10-11	007	A